見込み	a	b	c	d	e	△2 f	g △3	h △3 △2
NC95	95	67	14	47.5	31.5	67.5	32.5	62.5
NC115	115	67	24	57.5	37.5	77.5	42.5	72.5
NC140	140	67	36.5	70	50	90	55	85 △7
NC156	156	101	27.5	78	58	98	63	93
NC171	171	116	27.5	85.5	65.5	105.5	70.5	100.5
NC180	180	125	27.5	90	70	110	75	105

錠種類	錠位置	範囲	3方枠A p寸法	3方枠B p寸法
プッシュ錠	標準	H20	1056.5	1068.5
		628≦H＜1428	(H+255)/2	(H+279)/2
	△5	1428≦H≦2500	1056.5	1068.5


△4

△1 枠	H呼称	H	L	n	j	k	△6 r	△5 i	m	k'	m'
3方枠A	H20	2023	2023	3	200	905.5	0	717.5	200	917.5	188
	特注	628≦H＜1000	H	2	130	H−330	0	0	200	H−318	188
		1000≦H＜1478	H	2	200	H−400	0	0	200	H−388	188
	△5	1478≦H＜2426	H	3	200	H−1117.5	0	717.5	200	H−1105.5	188
		2426≦H≦2500	H	4	200	H−1835	717.5	717.5	200	H−1823	188
3方枠B	H20	2023	2035	3	200	917.5	0	717.5	200	929.5	188
	特注	628≦H＜1000	H+12	2	130	H−318	0	0	200	H−306	188
		1000≦H＜1478	H+12	2	200	H−388	0	0	200	H−376	188
	△5	1478≦H＜2426	H+12	3	200	H−1105.5	0	717.5	200	H−1093.5	188
		2426≦H≦2500	H+12	4	200	H−1823	717.5	717.5	200	H−1811	188


【上部】

△3【下部:3方枠A】※注2

△3【下部:3方枠B】※注2

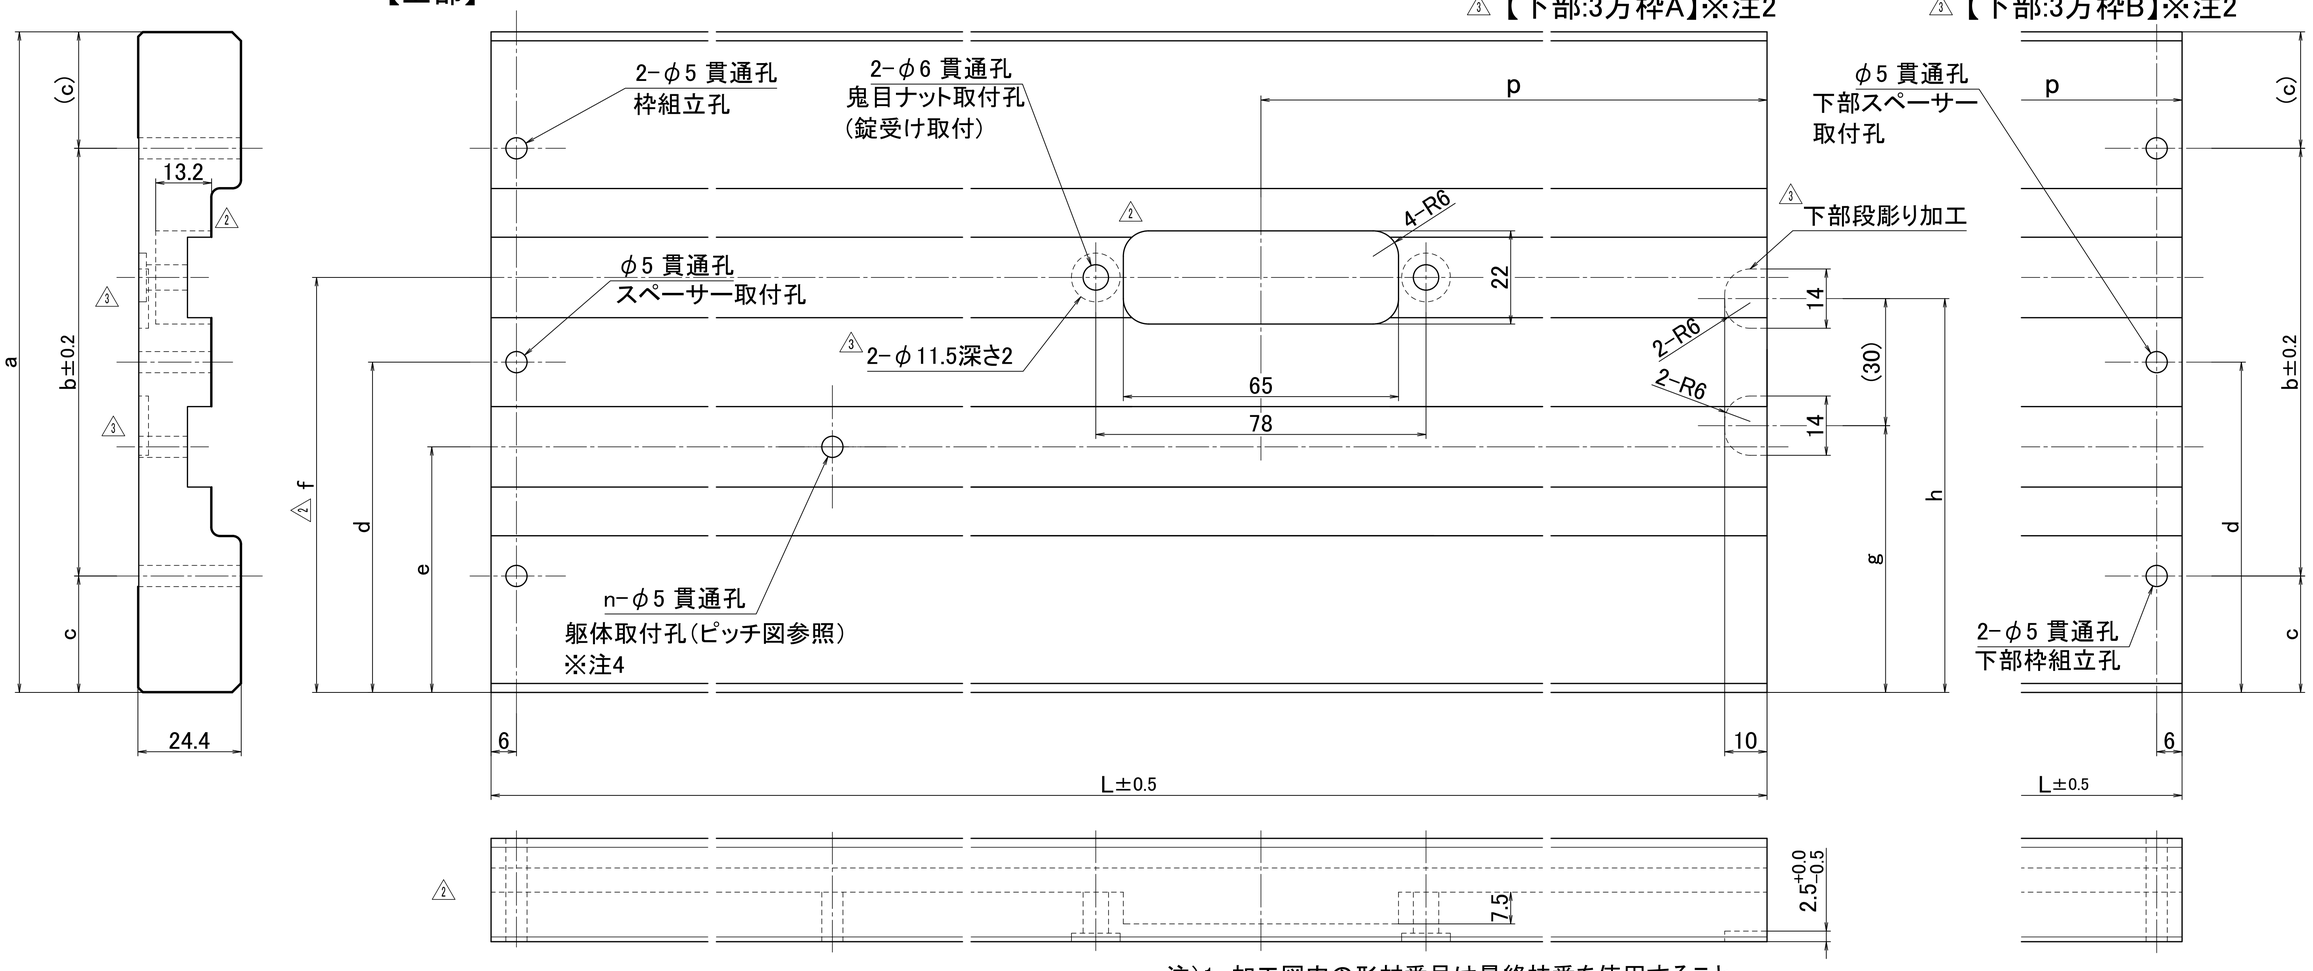

【躯体取付孔ピッチ図】

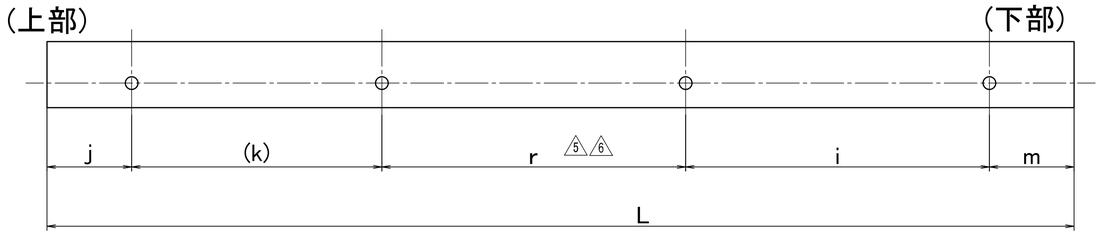

注)1. 加工図内の形材番号は最終枝番を使用すること。

△3 △1 2. 下部の加工は下記のとおりとする。
3方枠A:下部段彫り加工
3方枠B:下部枠組立孔、下部スペーサー取付孔

3. ピッチ図k、mは寸法表のk'、m'に置き換えても可とする。

4. NC95のみ躯体取付孔加工は戸当り溝センターから外れた加工とする。

△2 5. 錠加工は特注対応とし、引違2枚の場合のみ対応する。

	縦枠NC180		MDF+HPJシート	MD-07683	
	縦枠NC171		MDF+HPJシート	MD-07682	
	縦枠NC156		MDF+HPJシート	MD-07681	
	縦枠NC140		MDF+HPJシート	MD-09294	△7
	縦枠NC115		MDF+HPJシート	MD-07680	
	縦枠NC95		MDF+HPJシート	MD-07679	
番号	名称	員数	材質・規格	部品図番	備考

改訂 記号	年月日	担当	変更理由
△7 −2	24/10/31	靖超	設指TJ-3086 NC140追加
△6 −2	23/08/03	松尾ひかる	設指TJ-2863 誤記訂正
△5 −5	22/09/30	車文華	設指TJ-2571 H25特注対応

仕上 / 熱処 / 表処 / 公差

尺度	1/1	日付	16/06/22	承認	梶原	検図	鈴木荘右	佐藤淳一	設計	佐藤淳一	製図	孫挺
角法	三角法											

名称 H310 17ラシッサ V引違戸2/4枚建 枠 縦枠 加工図

株式会社 LIXIL 図番 H310C10043

承認日:2024/11/29

「(株)LIXIL化学物質管理ランク指針」を順守すること。
The used material must follow the List of the Environment-Related Substances to be controlled by LIXIL Corporation.