
見込み	a	b	c
NC95	92	67	12.5
NC115	110	67	21.5
NC140 △1	135	67	34
NC156	151	101	25
NC171	166	116	25
NC180	175	125	25

品種	呼称	W	L
引違戸2枚建	W16	1644	1596
	W18	1824	1776
引違戸4枚建	W32	3253	3205

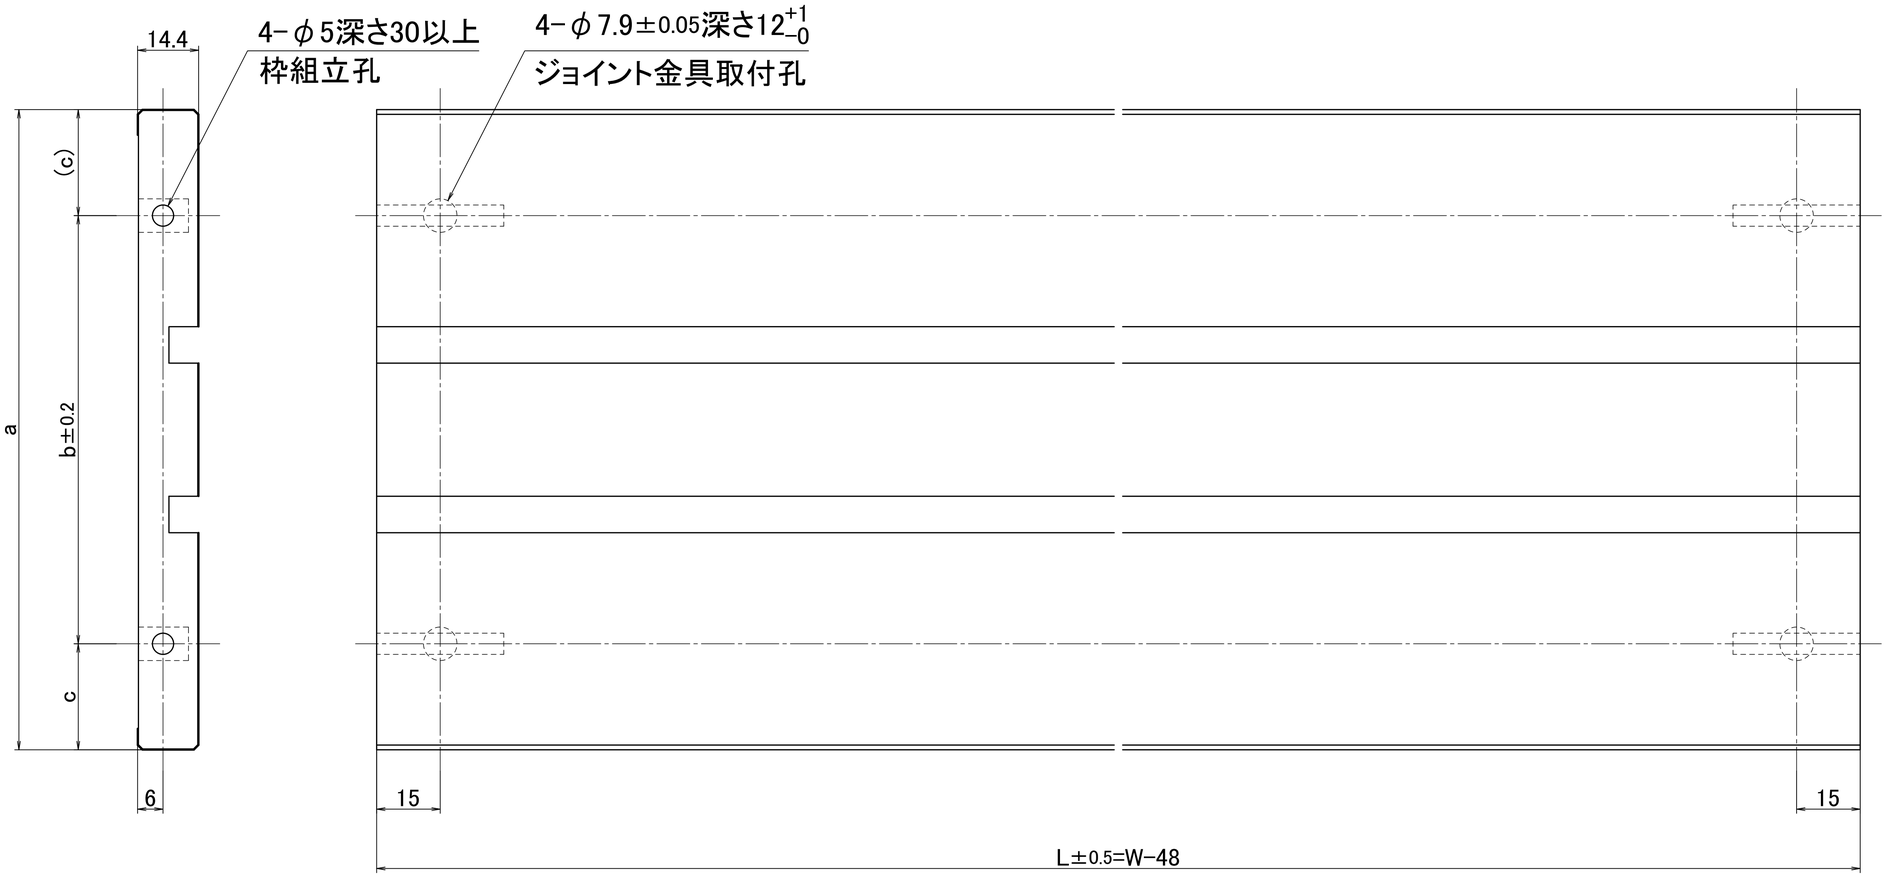

注)1. 加工図内の形材番号は最終枝番を使用する事。

	つば無薄敷居NC180		MDF+HPJシート	MD-07690	
	つば無薄敷居NC171		MDF+HPJシート	MD-07689	
	つば無薄敷居NC156		MDF+HPJシート	MD-07688	
△1	つば無薄敷居NC140		MDF+HPJシート	MD-08132	
	つば無薄敷居NC115/C付薄壁		MDF+HPJシート	MD-07687	
	つば無薄敷居NC95		MDF+HPJシート	MD-07686	
番号	名称	員数	材質・規格	部品図番	備考

改訂 記号	年月日	担当	変更理由
△			設指
△1 -2	24/10/31	唐楊	設指TJ-3086 見込み追加
△	16/07/29	孫挺	設指TH-9963 新規出図

仕上	熱処	表処	公差

尺度	1/1	日付	16/06/23	承認	梶原	検図	鈴木荘右	佐藤淳一	設計	佐藤淳一	製図	孫挺
角法	三角法			名称	H310 17ラシッサ V引違戸2/4枚建 枠 薄敷居 加工図							
株式会社 LIXIL				図番	H310C10052							

承認日:2024/11/29

「(株)LIXIL化学物質管理ランク指針」を順守すること。
The used material must follow the List of the Environment-Related Substances to be controlled by LIXIL Corporation.