
見込み	a	b	c
NC95	76	18	29
NC115/C付	96	62	17
NC140 ⚠1	89	18	35.5
NC156	105	62	21.5
NC171/NC180	120	62	29

品種	呼称	W	L
引違戸2枚建	W16	1644	1596
	W18	1824	1776
引違戸4枚建	W32	3253	3205

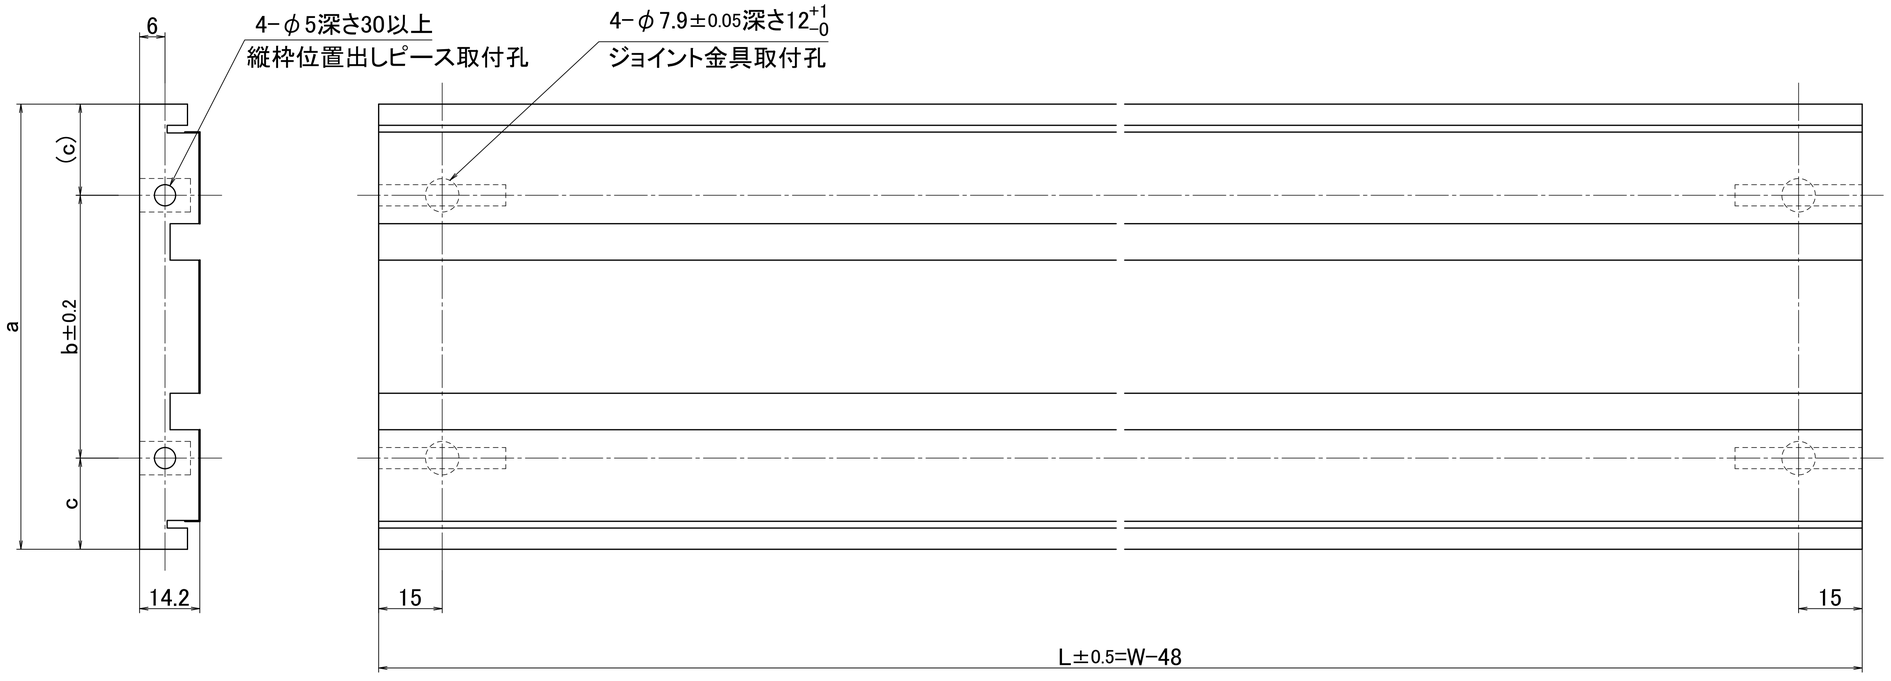

注)1. 加工図内の形材番号は最終枝番を使用する事。

	番号	名称	員数	材質・規格	部品図番	備考
		つば付薄敷居NC171/NC180		MDF+HPJシート	MD-07695	
		つば付薄敷居NC156		MDF+HPJシート	MD-07694	
⚠1		つば付薄敷居NC140		MDF+HPJシート	MD-09295	
		つば付薄敷居NC115/C付		MDF+HPJシート	MD-07693	
		つば付薄敷居NC95		MDF+HPJシート	MD-07692	

改訂	記号	年月日	担当	変更理由
△				設指
⚠1 −2		24/10/31	唐楊	設指TJ-3086 見込み追加
△		16/07/29	孫挺	設指TH-9963 新規出図

仕上	熱処	表処	公差

尺度	1/1	日付	16/06/23	承認	梶原	検図	鈴木荘右	佐藤淳一	設計	佐藤淳一	製図	孫挺
角法	三角法										名称	H310 17ラシッサV引違戸2/4枚建 枠 ツバ付薄敷居 加工図
株式会社 LIXIL											図番	H310C10058

「(株)LIXIL化学物質管理ランク指針」を順守すること。
The used material must follow the List of the Environment-Related Substances to be controlled by LIXIL Corporation.

承認日:2024/11/29