
枠種類	呼称	W	L
片引戸	W12	1188	1139
	W13	1324	1275
	W14	1454	1405
	W16	1644	1595
	W18	1824	1775
片引戸2枚建	W24	2432	2383
片引戸3枚建	W32	3220	3171

枠種類	呼称	W	L
引違戸2枚建	W16	1644	1595
	W18	1824	1775
引違戸3枚建	W24	2432	2383
引違戸4枚建	W32	3253	3204
引分戸	W32	3253	3204

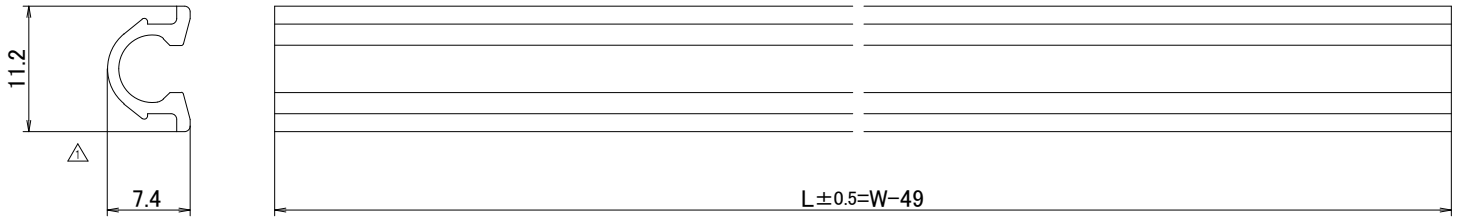

注)1. 加工図内の形材番号は最終枝番を使用する事。

「株式会社ＬＩＸＩＬ使用管理物質一覧表」を順守すること。
The used material must follow the List of the Environment-Related Substances to be controlled by LIXIL Corporation.

仕上		熱処		表処		公差	

改訂	記号	年月日	担当	変更理由
△				設指
1 -1		16/12/02	保泉明	設指 TJ-0154 Vレール形状変更
△		16/07/29	王寛	設指 TH-9963 新規出図

番号	名称	員数	材質・規格	部品図番	備考
	Vレール		AL	TO-4L047	

尺度	2/1	日付	16/06/29	承認	黒石	検図	鈴木荘右		佐藤淳一	設計	佐藤淳一	製図	王寛
角法	三角法			名称	H310 17ラシッサ V引戸 枠 Vレール 加工図								
株式会社 LIXIL				図番	H310C10064								

承認日:2016/12/02