

《 中縦枠 溝カバー材 取付要領図 》

中縦枠の溝へカバー材を嵌め込む。(圧入する)

注)1. カバー材の割れが無いこと。
2. カバー材の浮きが0.5mm未満であること。(A部詳細参照)
3. カバー材嵌め込み時、モヘアの巻き込みは可とする。
4. カバー材は下端部切欠き(中縦枠下部ピース)に合わせて取り付けること。

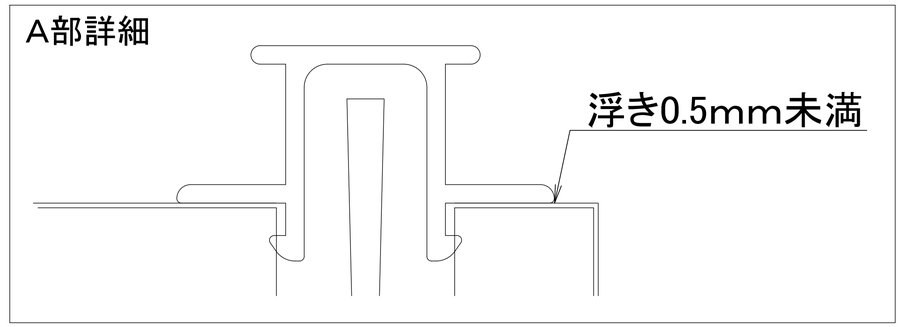

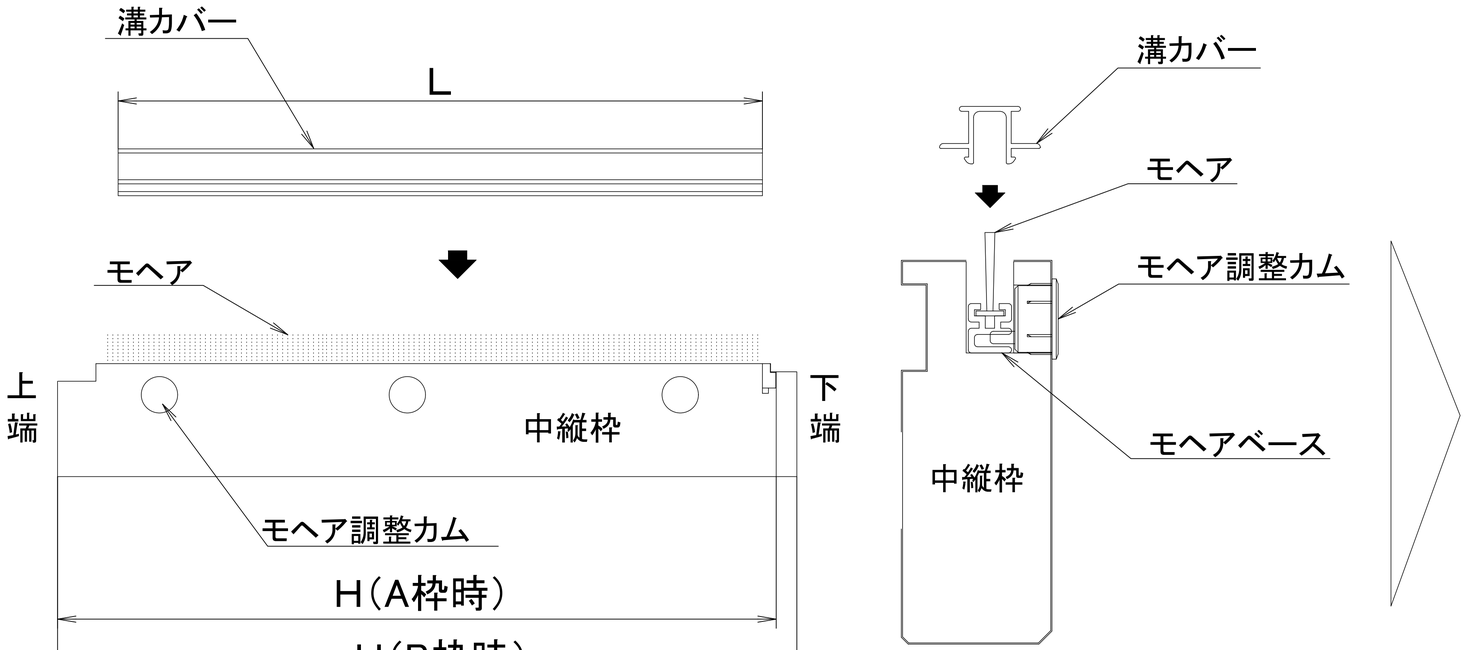

カバー嵌め込み後完成図

中縦枠溝カバー材 特寸時使い分け表
※H≦1855についてはカバー取付不要。

H	L	部品コード
1855<H≦1950	1815	MEA996L4
1950<H≦2045	1910	MEA996L5
2045<H≦2140	2005	MEA996L6
2140<H≦2235	2100	MEA996L7
2235<H≦2330	2195	MEA996L8
2330<H≦2425	2290	MEA996L9
2425<H≦2500	2385	MEA996L3

△	. .		△	. .	
△	. .		△	. .	
△	. .		△	. .	
△	. .		△1 -1	22.09.30	TJ-2571 H25特注対応
△1	. .		△	20.01.31	TJ-1611新規出図

日付	20.01.31	承認	中野	審査		作成	木村圭佑
名称	H310 V片引戸/2/3枚建/V引分戸 枠 中縦枠溝カバー材取付要領図(E部)						
図番	H310U10035						

株式会社 LIXIL

承認日:2022/09/27