

見込み	a	b	c	d
NC95	92	67	12.5	26
NC115	110	67	21.5	35
NC140	135	67	34	47.5
NC156	151	101	25	55.5
NC171	166	116	25	63
NC180	175	125	25	67.5

呼称	W	L	e	n
W16	1644	1596	396	4
W18	1824	1776	126	5
特注	1188≦W＜1299	W-48	W-798	3
	1299≦W＜1749		W-1248	4
	1749≦W＜2199		W-1698	5
	2199≦W≦2412		W-2148	6

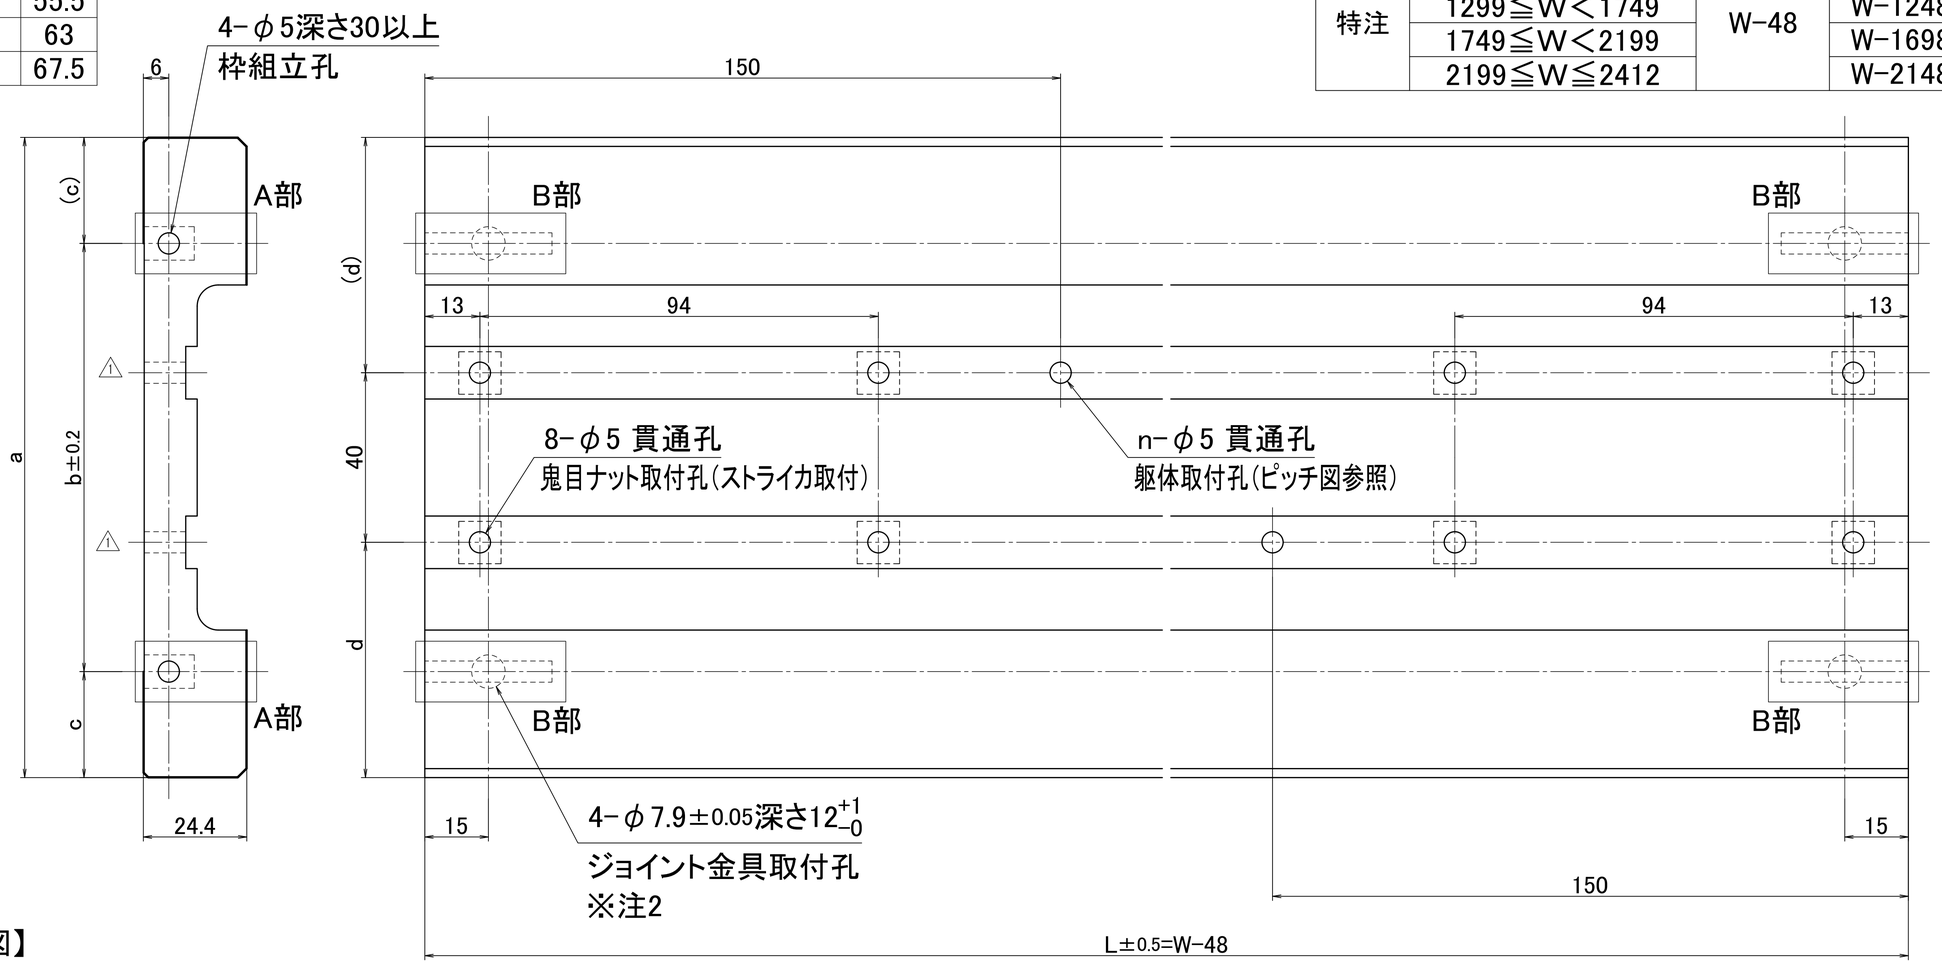


【躯体取付孔ピッチ図】


1188≦W＜1299

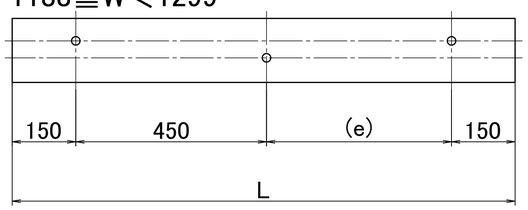


1299≦W＜1749

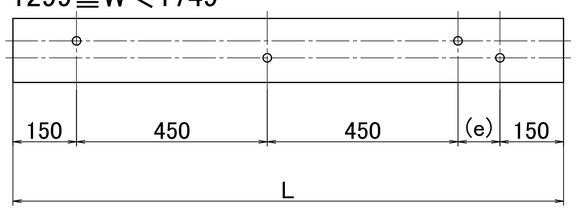


2199≦W≦2412

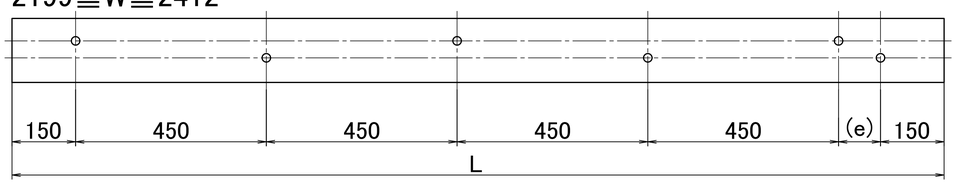

1749≦W＜2199

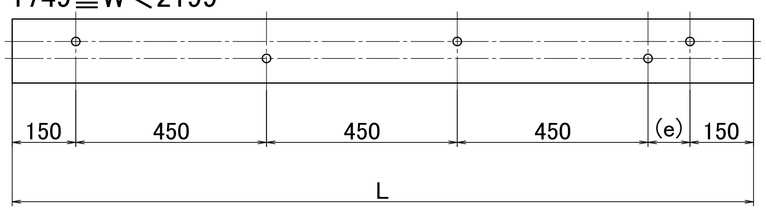

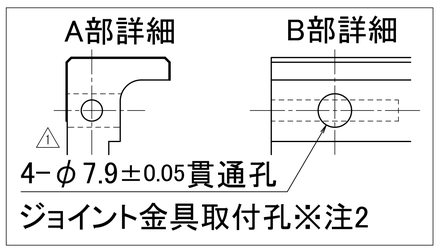

注)1. 加工図内の形材番号は最終枝番を使用する事。
2. NC95/115/140の場合、ジョイント金具取付孔は貫通孔とする。A、B部詳細を参照すること。

	鴨居NC180		MDF+HPJシート	MD-07676	
	鴨居NC171		MDF+HPJシート	MD-07675	
	鴨居NC156		MDF+HPJシート	MD-07674	
	鴨居NC140		MDF+HPJシート	MD-08614	△2
	鴨居NC115		MDF+HPJシート	MD-07673	
	鴨居NC95		MDF+HPJシート	MD-07672	
番号	名称	員数	材質・規格	部品図番	備考

改訂	記号	年月日	担当	変更理由
	△2 -3	24/10/31	靖超	設指TJ-3086 NC140追加
	△1 -3	17/02/03	高芳	設指TJ-0056 裏面溝削除
	△	16/07/29	孫挺	設指TH-9963 新規出図

尺度	1/1	日付	16/06/24	承認	梶原	検図	鈴木荘右	設計	佐藤淳一	製図	孫挺
角法	三角法										

名称 H310 17ラシッサ V引違戸2枚建 Wモーション 枠 鴨居 加工図

株式会社 LIXIL　図番 H310C10018

承認日:2024/11/29

仕上　熱処　表処　公差

「(株)LIXIL化学物質管理ランク指針」を順守すること。
The used material must follow the List of the Environment-Related Substances to be controlled by LIXIL Corporation.