

呼称	W	L	e	n
W16	1644	1595	396	4
W18	1824	1775	126	5
特注	732≦W＜849	W-49	W-348	2
	849≦W＜1299		W-798	3
	1299≦W＜1749		W-1248	4
	1749≦W＜2199		W-1698	5
	2199≦W≦2412		W-2148	6

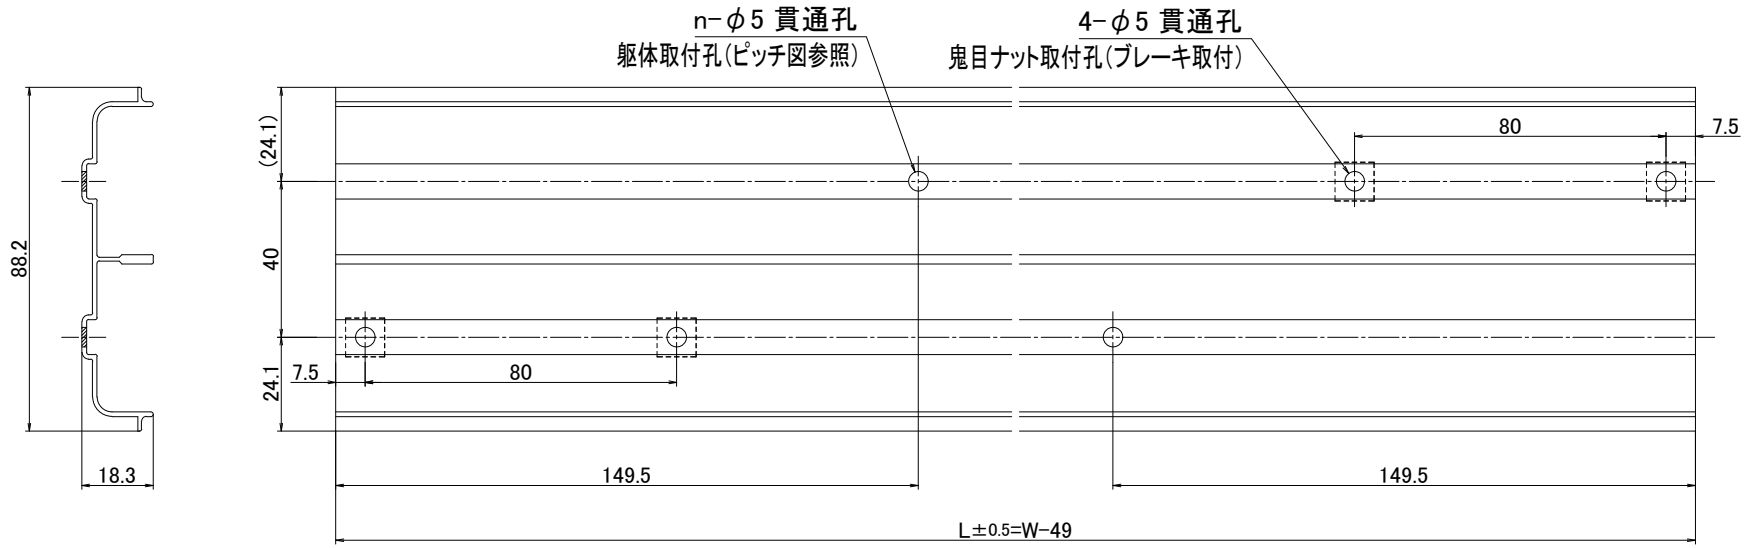


注)1. 加工図内の形材番号は最終枝番を使用する事。

【躯体取付孔ピッチ図】


732≦W＜849

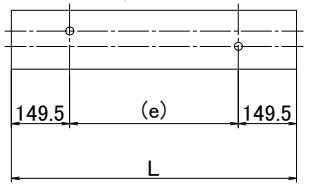


1299≦W＜1749

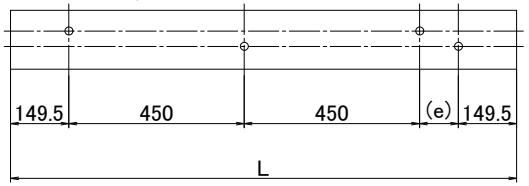


2199≦W≦2412

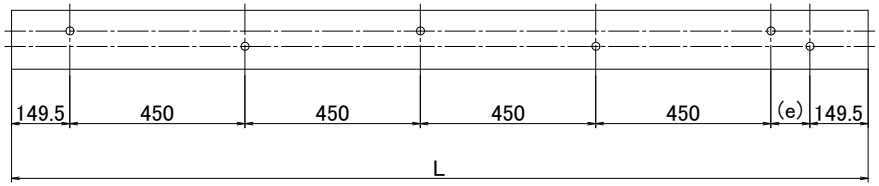

849≦W＜1299

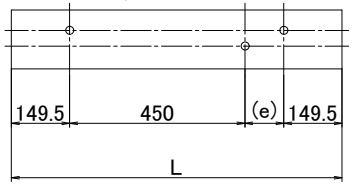

1749≦W＜2199

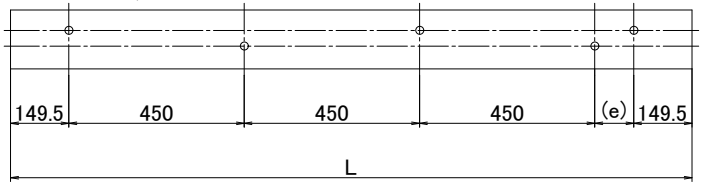

「株式会社ＬＩＸＩＬ使用管理物質一覧表」を順守すること。
The used material must follow the List of the Environment-Related Substances to be controlled by LIXIL Corporation.

仕上	-	熱処	-	表処	-	公差	-

改訂	記号	年月日	担当	変更理由
△			設指	
△			設指	
△		16/07/29	孫挺	設指 TH-0963 新規出図

	番号	名称	員数	材質・規格	部品図番	備考
		鴨居レール		AL	TO-5R775	

尺度	1/1	日付	16/06/24	承認	黒石	検図	鈴木荘右	設計	佐藤淳一	製図	孫挺
角法	三角法			名称	H310 17ラシッサ V引違戸2枚建 戸先ブレーキ 枠 鴨居レール 加工図						
株式会社 LIXIL				図番	H310C10025						

承認日:2016/07/29