

見込み	a	b	c	d
NC95	92	67	12.5	26
NC115	110	67	21.5	35
NC140	135	67	34	47.5
NC156	151	101	25	55.5
NC171	166	116	25	63
NC180	175	125	25	67.5

△2

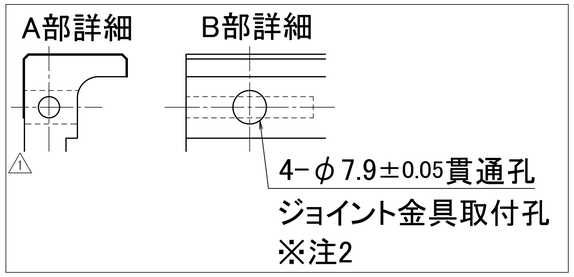


呼称	W	L	e	n
W16	1644	1596	396	4
W18	1824	1776	126	5
特注	732≦W＜849	W−48	W−348	2
	849≦W＜1299		W−798	3
	1299≦W＜1749		W−1248	4
	1749≦W＜2199		W−1698	5
	2199≦W≦2412		W−2148	6

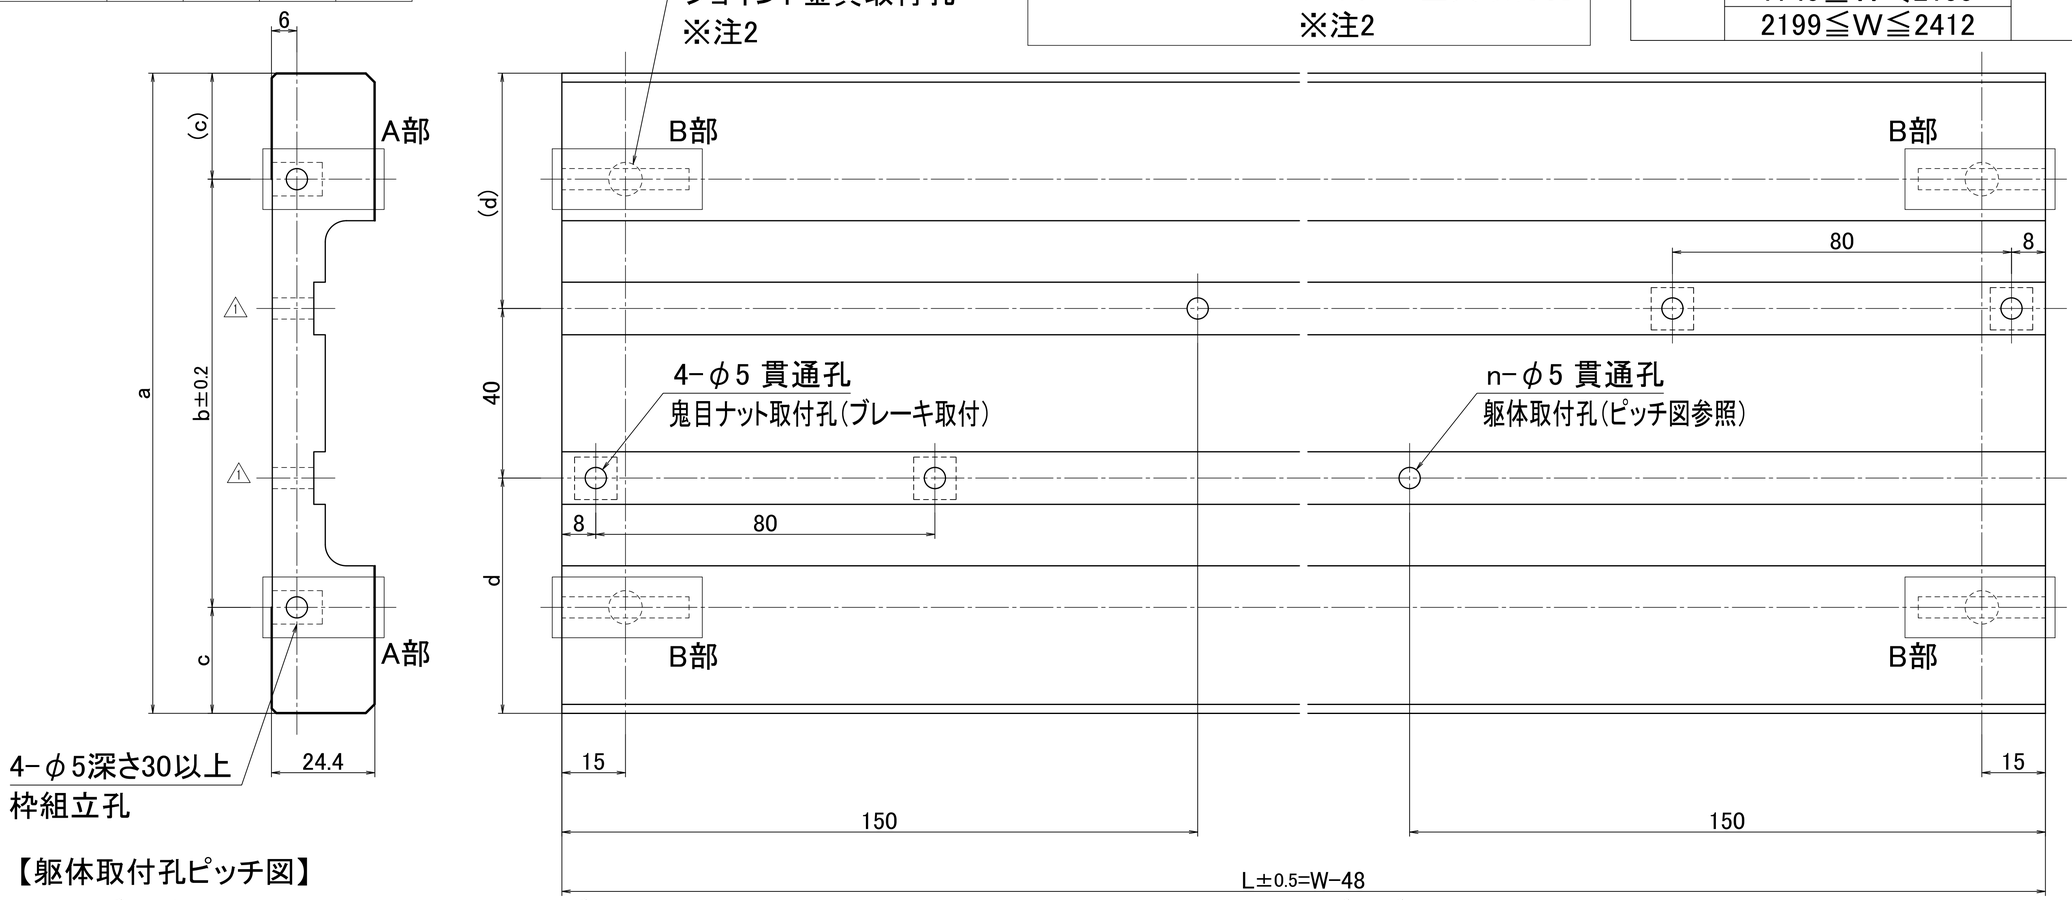


【躯体取付孔ピッチ図】


732≦W＜849

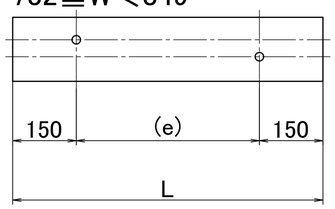


1299≦W＜1749

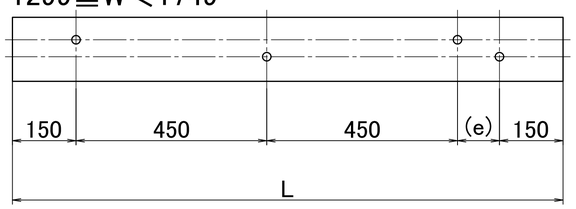


2199≦W≦2412

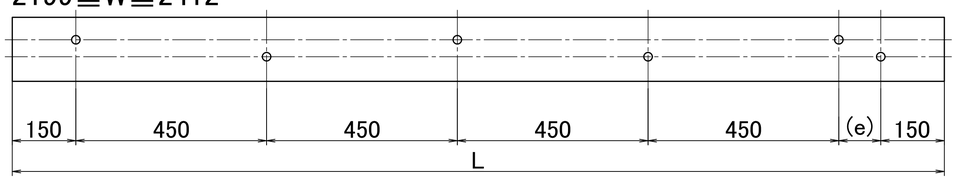

849≦W＜1299

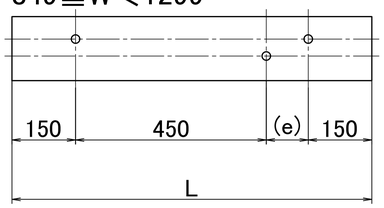

1749≦W＜2199

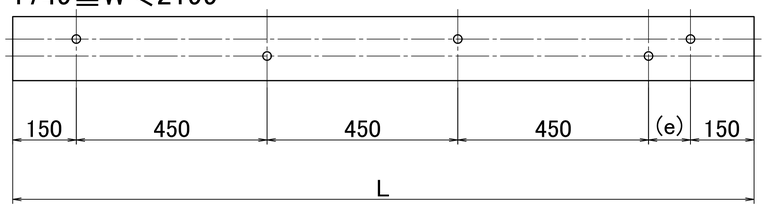

注)1. 加工図内の形材番号は最終枝番を使用する事。

2. △2 NC95/115/140の場合、ジョイント金具取付孔は貫通孔とする。
A、B部詳細を参照すること。

番号	名称	員数	材質・規格	部品図番	備考
	鴨居NC180		MDF+HPJシート	MD-07676	
	鴨居NC171		MDF+HPJシート	MD-07675	
	鴨居NC156		MDF+HPJシート	MD-07674	
	鴨居NC140		MDF+HPJシート	MD-08614	△2
	鴨居NC115		MDF+HPJシート	MD-07673	
	鴨居NC95		MDF+HPJシート	MD-07672	

改訂	記号	年月日	担当	変更理由
	△2 -3	24/10/31	靖超	設指TJ-3086 NC140追加
	△1 -3	17/02/03	高芳	設指TJ-0056 裏面溝削除
	△	16/07/29	孫挺	設指TH-9963 新規出図

仕上	熱処	表処	公差

尺度	角法	日付	承認	検図	設計	製図
1/1	三角法	16/06/24	梶原	鈴木荘右	佐藤淳一	佐藤淳一 孫挺

名称: H310 17ラシッサ V引違戸2枚建 戸先ブレーキ 枠 鴨居 加工図

株式会社 LIXIL

図番: H310C10004

承認日:2024/11/29

「(株)LIXIL化学物質管理ランク指針」を順守すること。
The used material must follow the List of the Environment-Related Substances to be controlled by LIXIL Corporation.